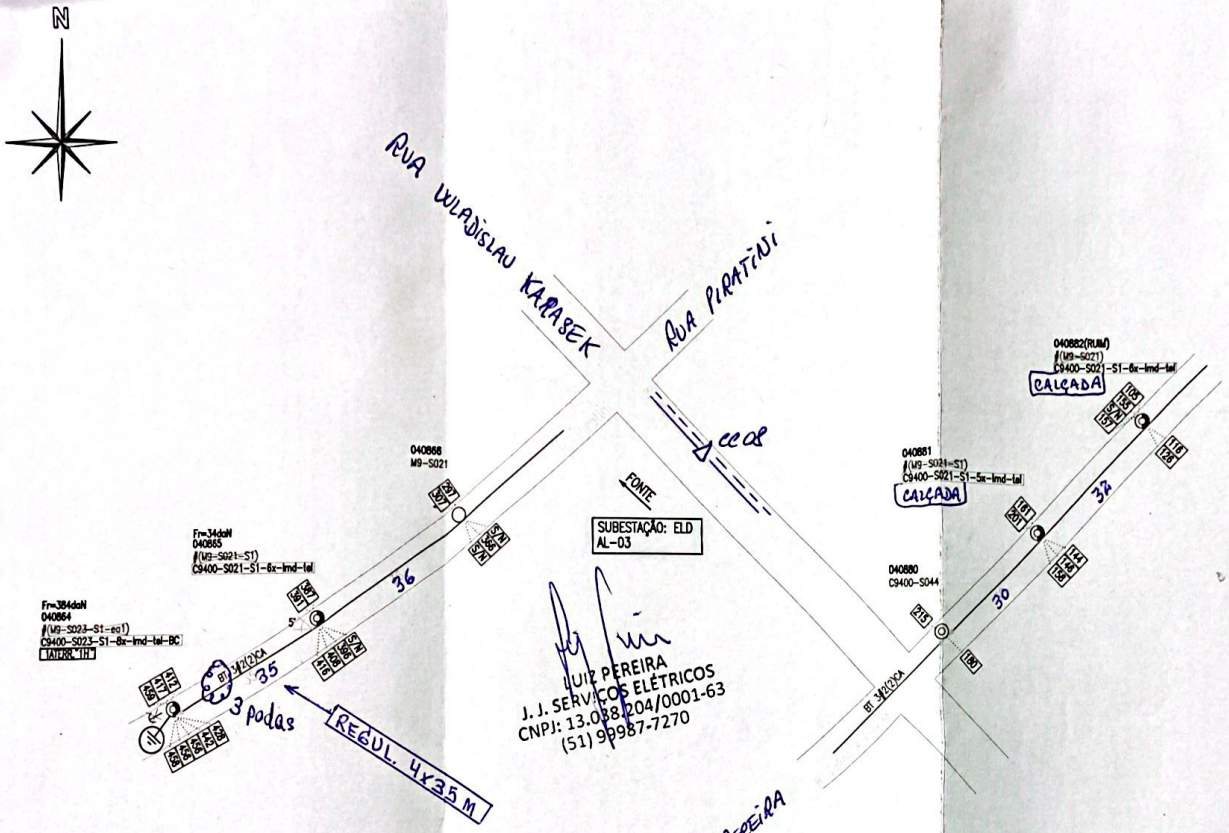

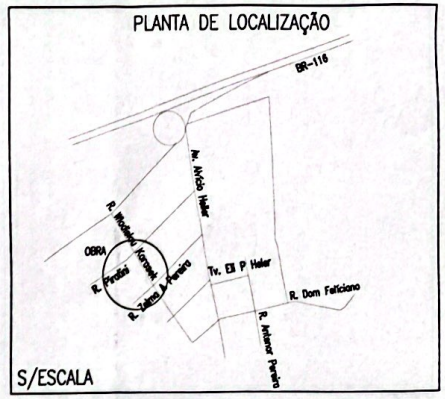

LUIZ PEREIRA
J. J. SERVIÇOS ELÉTRICOS
CNPJ: 13.038.204/0001-63
(51) 99987-7270

LEGENDA	
----	Rede de Alta Tensão
——	Rede de Baixa Tensão
○	Poste Existente Madeira
□	Poste Existente Duplo-T
■	Poste Projetado Duplo-T
◎	Poste Existente Tronco Cônico
◉	Poste Projetado Tronco Cônico
→	Estai de Âncora
	Aterramento Projetado
	Pára-raios Projetado
	TRS CEEE Projetado
	TRS Particular
	Estrutura Projetada
	Estrutura Retirada
	Consumidor Projetado
	Consumidor Existente
	Chave Fusível Projetada
	Haste Franklin Projetada

EI NOVO: RS-2202504MBT1.1.0014 ~~RES 1159478~~

CONDUTORES	INSTALADO (KM)	RETIRADO (KM)	TOTAL (KM)
TOTAL PROJETADO	-	-	0.000

Nº	DATA	1ª REVISÃO	FEITA	VER	PROJ.	VISTO	APR.

CEEE D

MBT - PROJETO DE MANUTENÇÃO DE SERVIÇO

Proenergia

CONTRATO Nº: CEEE-D/2018/5000002360

ART: 9514037 E 10717949

MUNICIPIO: ELDORADO DO SUL

PROJETO Nº: 136326-DBT/22.36326-

PROCESSO Nº: EI 1093733

ESCALA: 1:1000

DATA: 07/11/2022

FOLHA Nº: 1/1

CEEE EQUATORIAL
SUBSTITUIÇÃO DE POSTES
R. ZELMA A PEREIRA, 155

Téc. Resp:
Eng. Eletricista Gilson F. Ogando _____ CREA RS-11420-D

Scanned with CamScanner